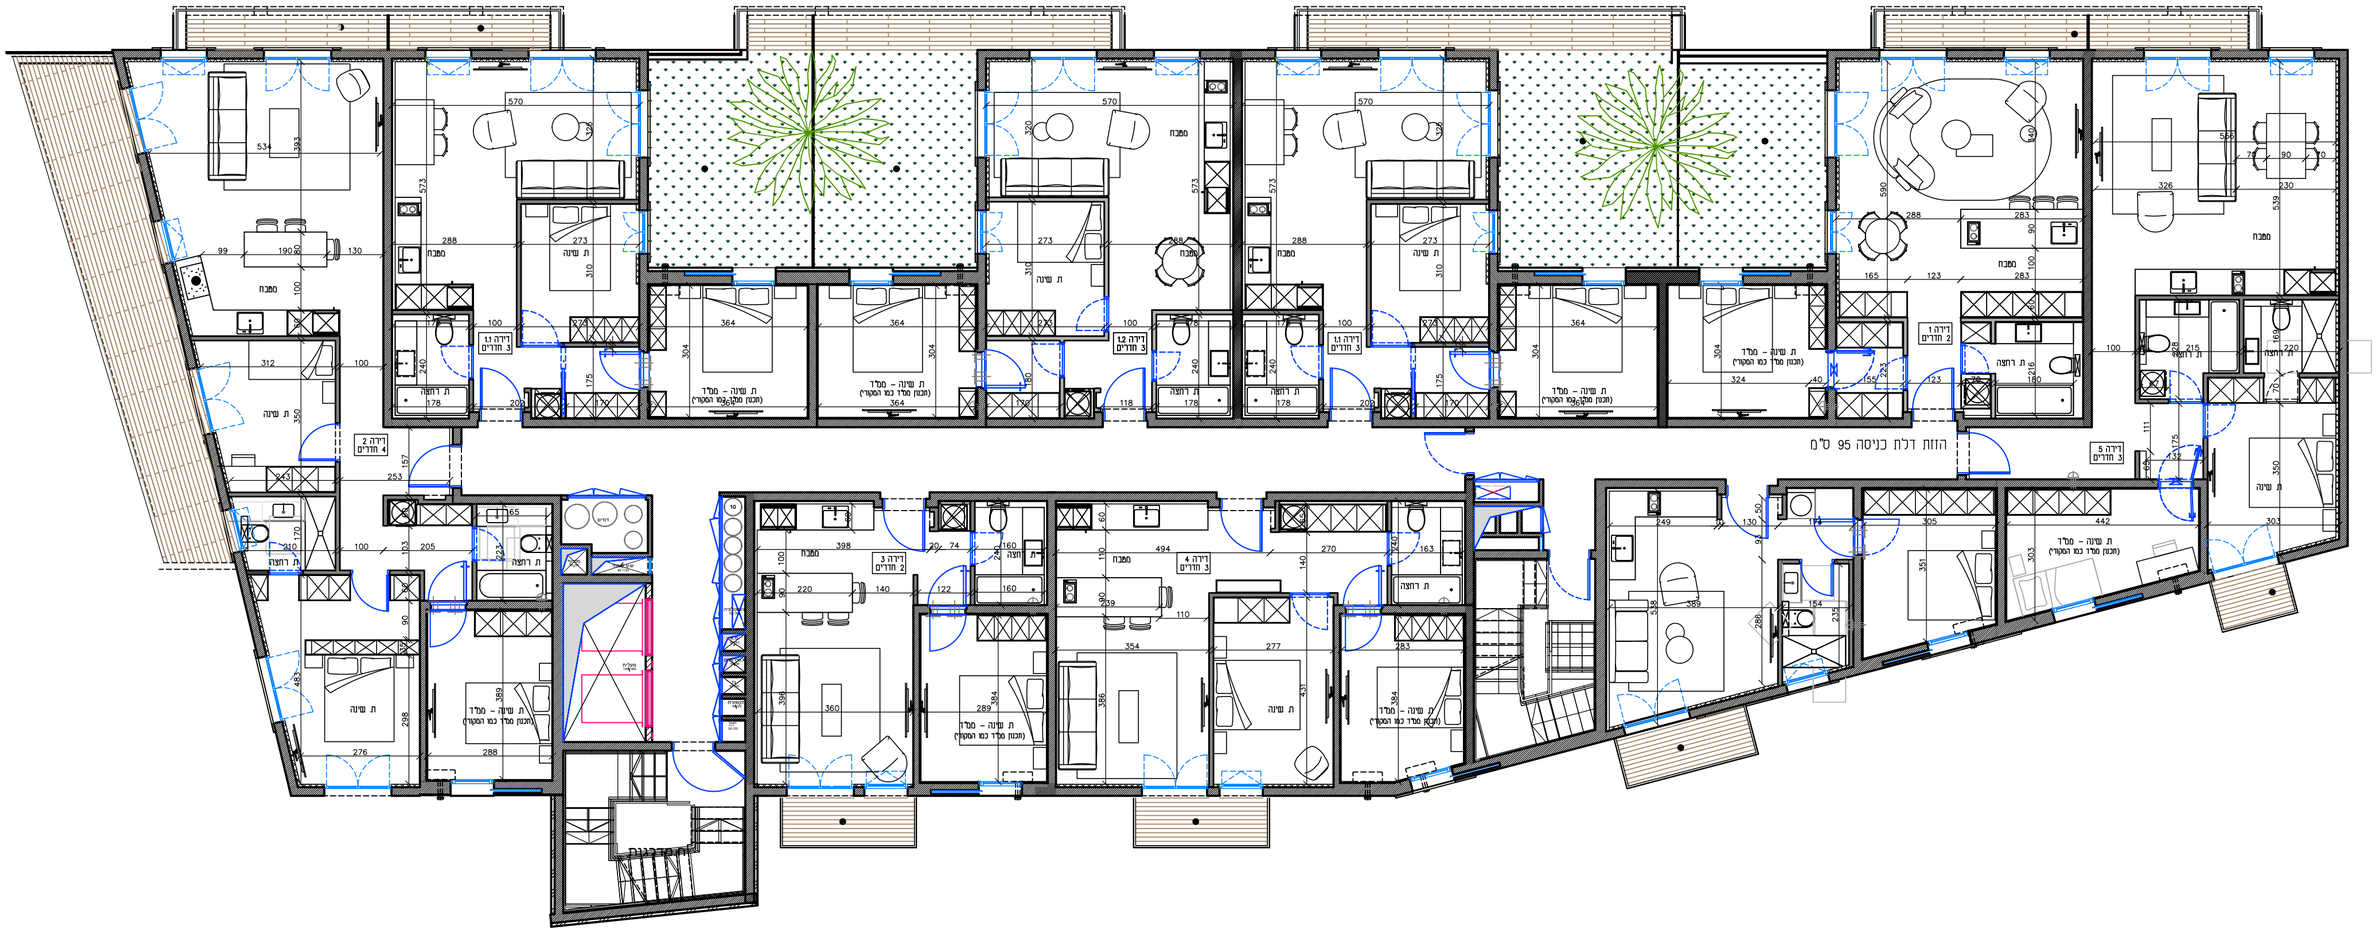

YARON ELDAD ARCHI TEC TURE +INTERIOR DESIGN	ירון אלדד ארכיטקטורה ועיצוב פנים כתובת: בנבנישתי 11 ת"א טלפון: 03-5335536\7 פקס: 03-5480136 yaroneldad.com	לעיון ○ לאישור ○ למכרז ○ לביצוע ●	על הקבלן לבקר את המידות, להתאימן לביצוע ולהודיע למתכנן על כל סטיות, סטיה, סתירה או אי התאמה בטרם ימשיך בעבודתו. המתכנן הינו הבעלים הבלעדי של תכנית זו ושל זכויות היוצרים בה. אין לעשות כל שימוש בתכנית זו, ברעיונות הגלומים בה ללא אישור מראש ובכתב של המתכנן.	תוכנית אדריכלות קומה א' – ריהוט מקרא: קירות בטון קירות גבס	הדואר 8
		קנ"מ: 1:100 תאריך: 09/04/2026 גודל גליון: כתובת: כתובת			