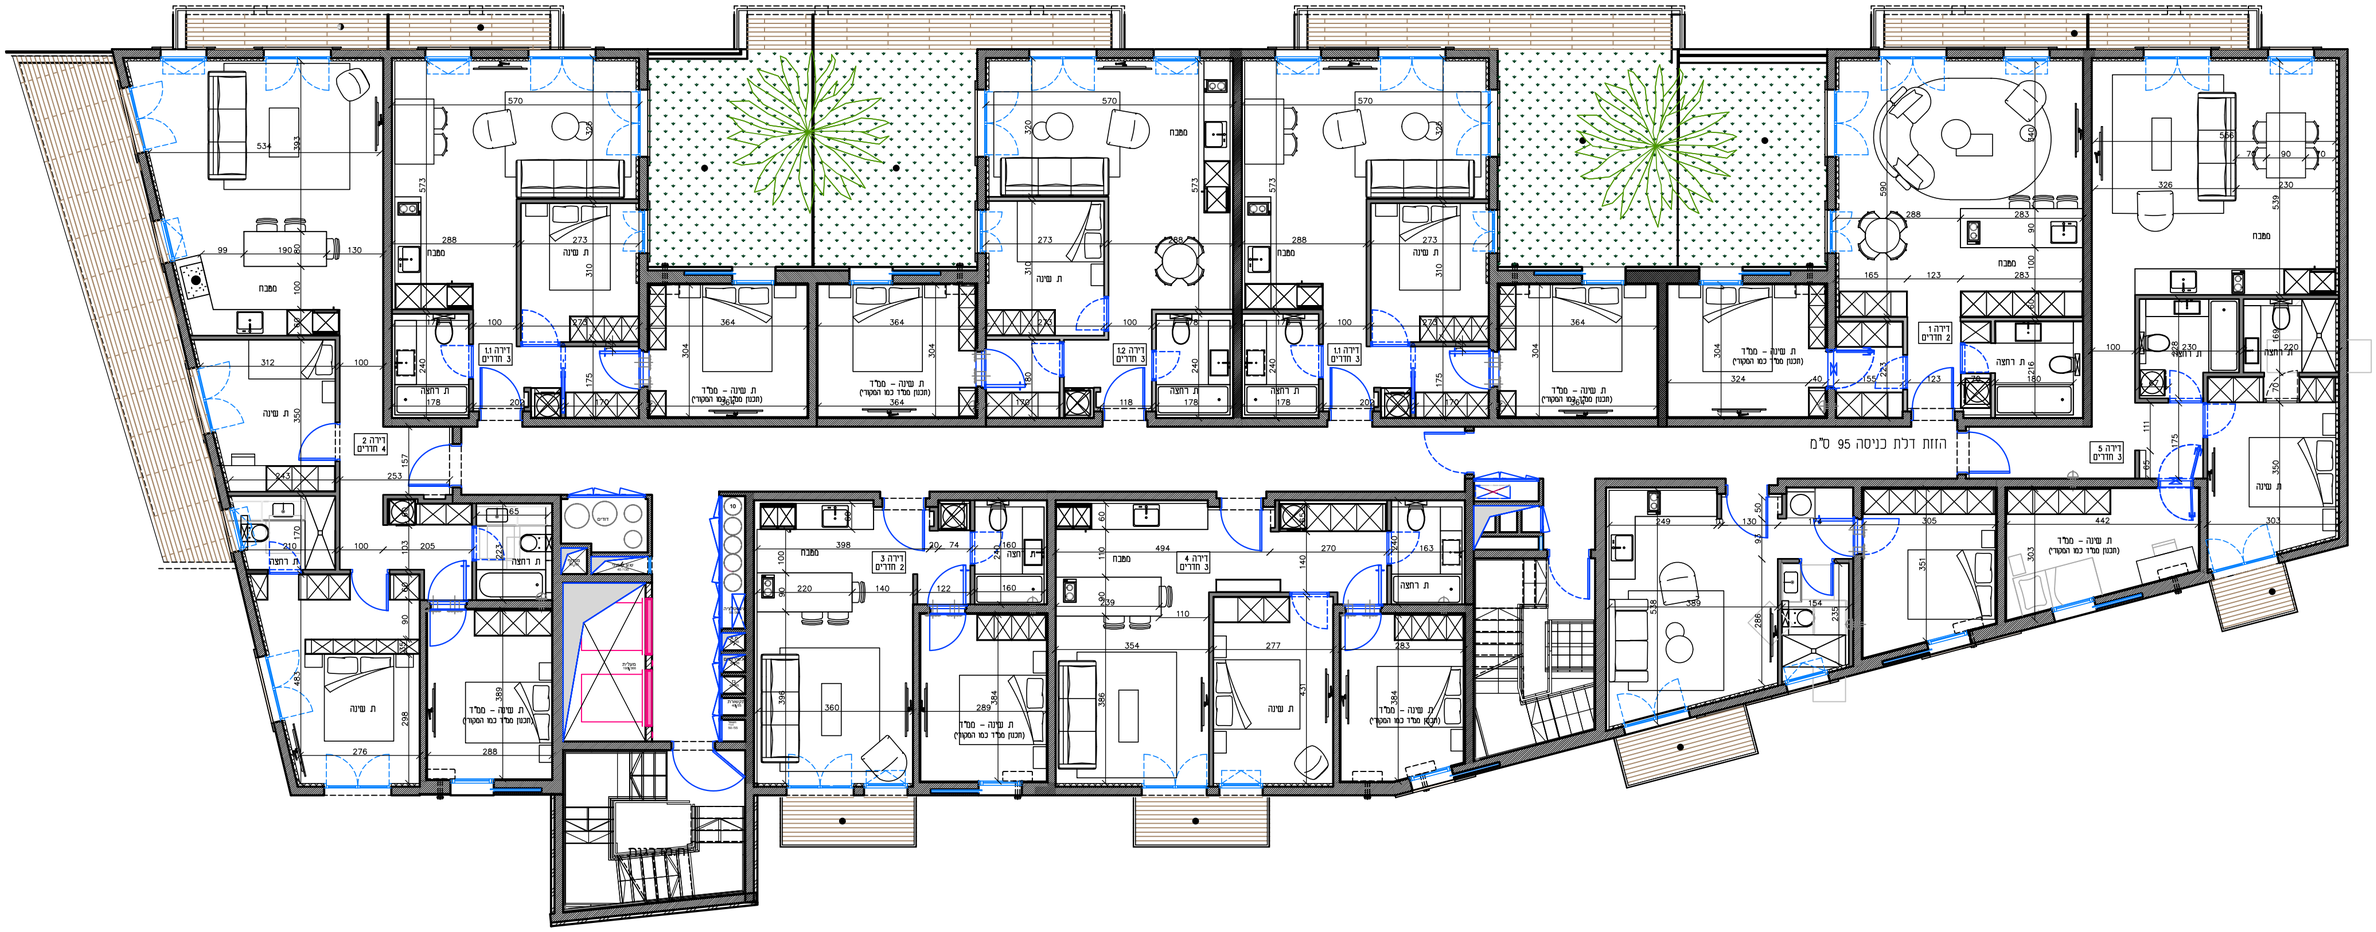

YARON ELDAD ARCHI TEC TURE +INTERIOR DESIGN	ירון אלדד ארכיטקטורה ועיצוב פנים כתובת: בנבנישתי 11 ת"א טלפון: 03-5335536\7 פקס: 03-5480136 yaroneldad.com	לביצוע ● למכרז ○ לאישור ○ לעיון ○ קנ"מ: 1:100 תאריך: 09/04/2026 גודל גליון: כתובת: כתובת	על הקבלן לבקר את המידות, להתאימן לביצוע ולהודיע למתכנן על כל טעות, סטיה, סתירה או אי התאמה בטרם ימשיך עבודתו. המתכנן הינו הבעלים הבלעדי של תכנית זו ושל זכולת היוצרים בה. אין לעשות כל שימוש בתכנית זו, ברעיונות הגלומים בה ללא אישור מראש ובכתב של המתכנן.	תוכנית אדריכלות קומה ב' – ריהוט מקרא: קירות בטון קירות גבס	הדואר 8		