


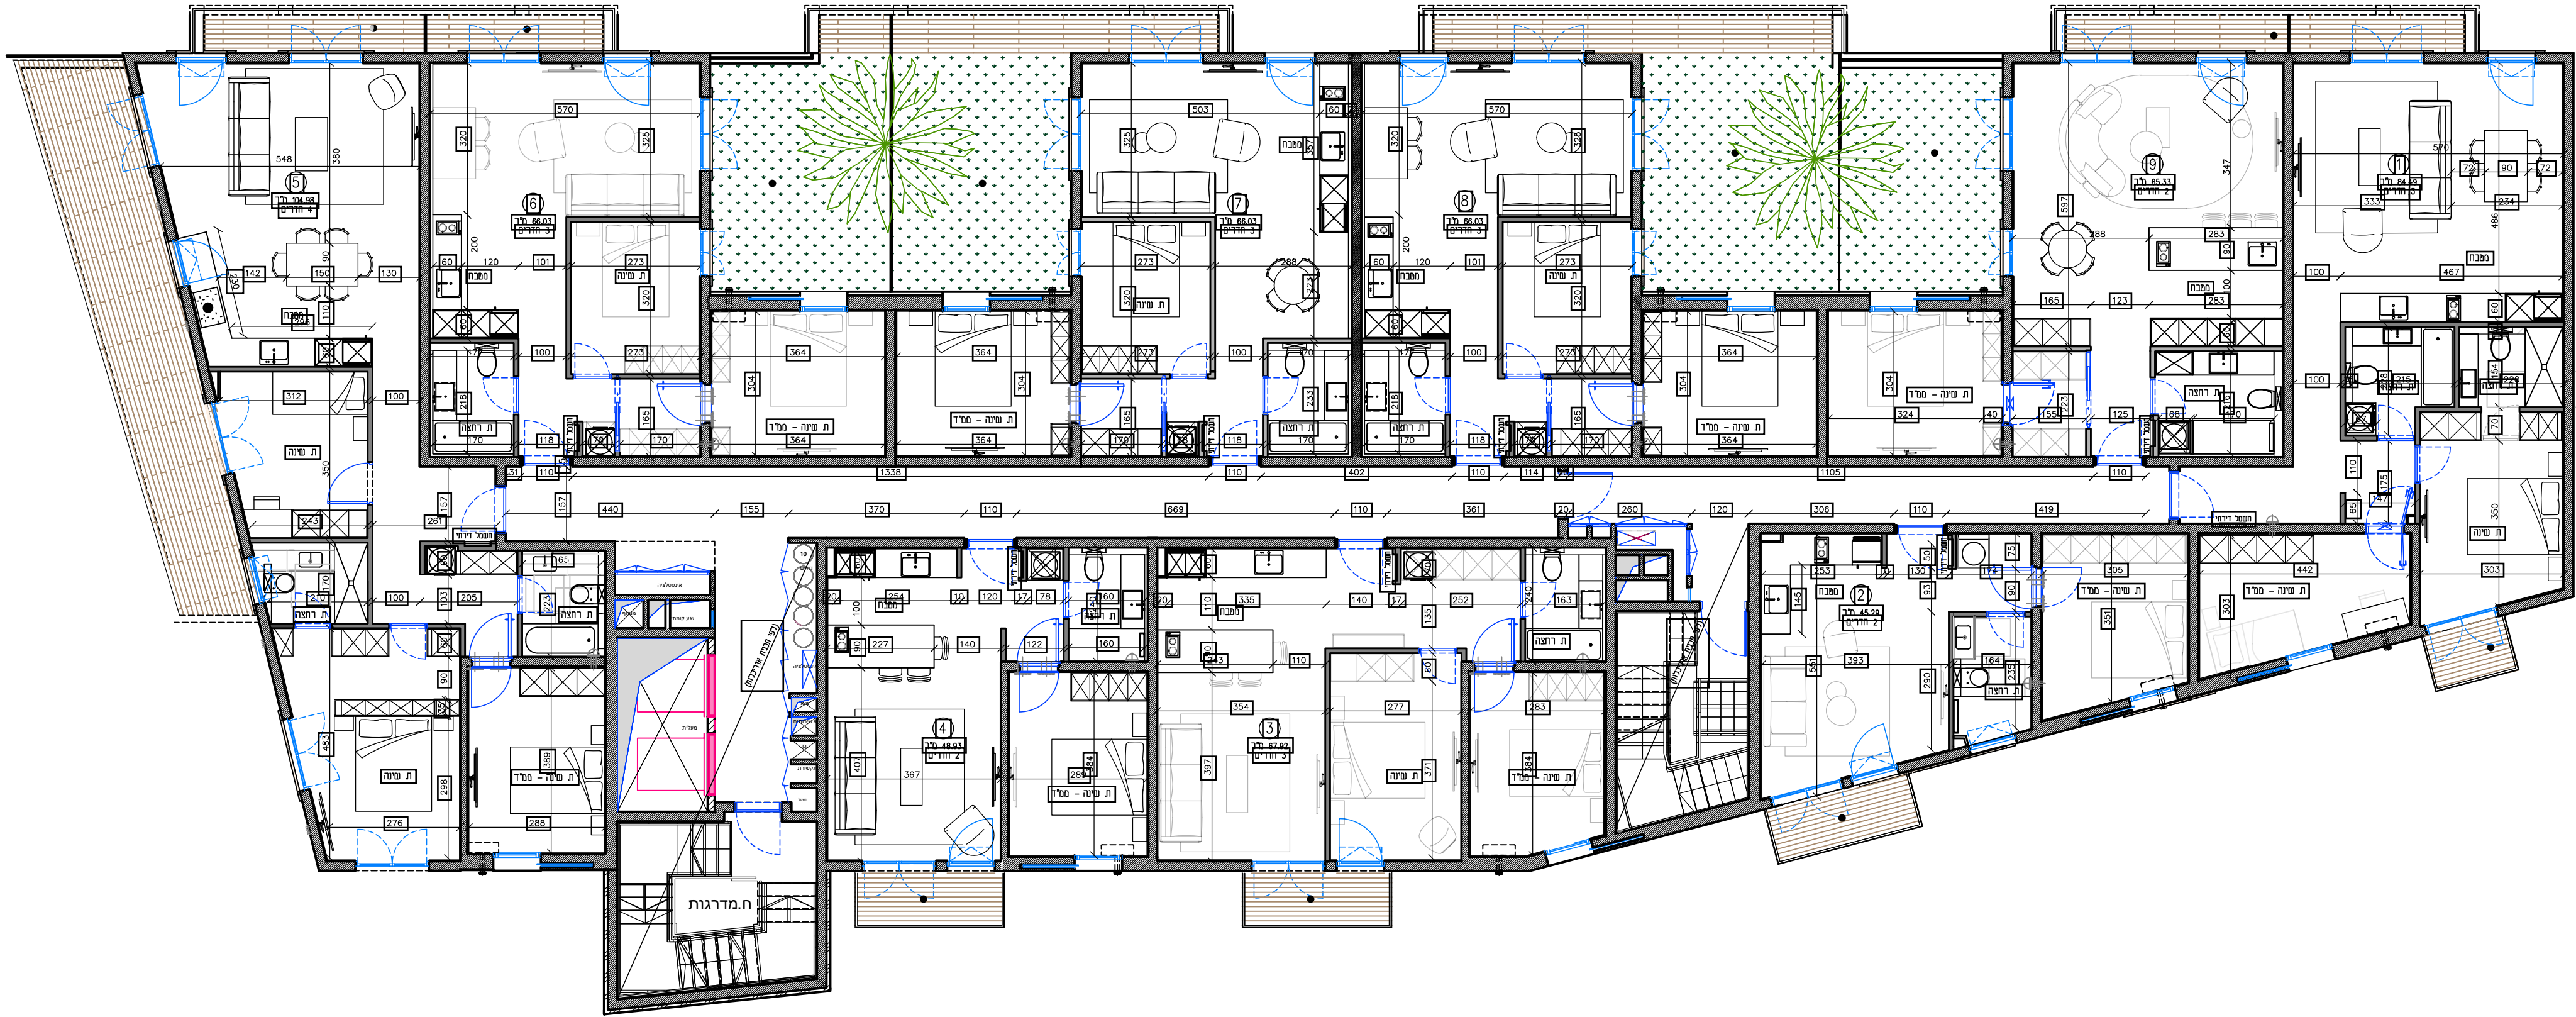

YARON
ELDAD
ARCHI
TEC
TURE
+INTERIOR
DESIGN

ירון אלדד
ארכיטקטורה ועיצוב פנים
כתובת: בובנישתי 11 ת"א
טלפון: 03-5335536/7
פקס: 03-5480136
yaroneldad.com

על הקבץ לבקר את המידות, להתאים ביצוע ולהודיע למחנך
על כל שעות, מספר, סחורה או אי התאמה בפרט ימשיך עבודתו
המחנך והעובדים הנבחרים של חכנית זו ועל זכות הוצאים בה
אין לעשות כל שימוש בחכנית זו, בפרטיות והגיוס בה
כל אישור מראש ונכתב על המחנך.


מקרא:
קירות גבס/בלוקים
קירות חוק
עמודים

ענייניים
תאריך
07/07/2026
הזאת דלתות חדרי שינה

כביצוע
למכרז
כאישור
לעיון

הפצה
סחורה
ידון אינד אוריכל
מנהל פרויקט
קונסטרוקציה
יועץ תכנון
אישור ציור
מיון איר
חשבוט
ביור, אשם ואקוסטיקה
בשיחוח
מעכית
יועץ גילא
יועץ גישות
קבץ

תאריך: 07/07/2026
מחזור: 2
קני"מ: 1:100
גודל גליון: A2
שם הפרויקט: הדואר 8
כתובת: יפו - תל אביב
שם התוכנית: קומה א - דירה 8

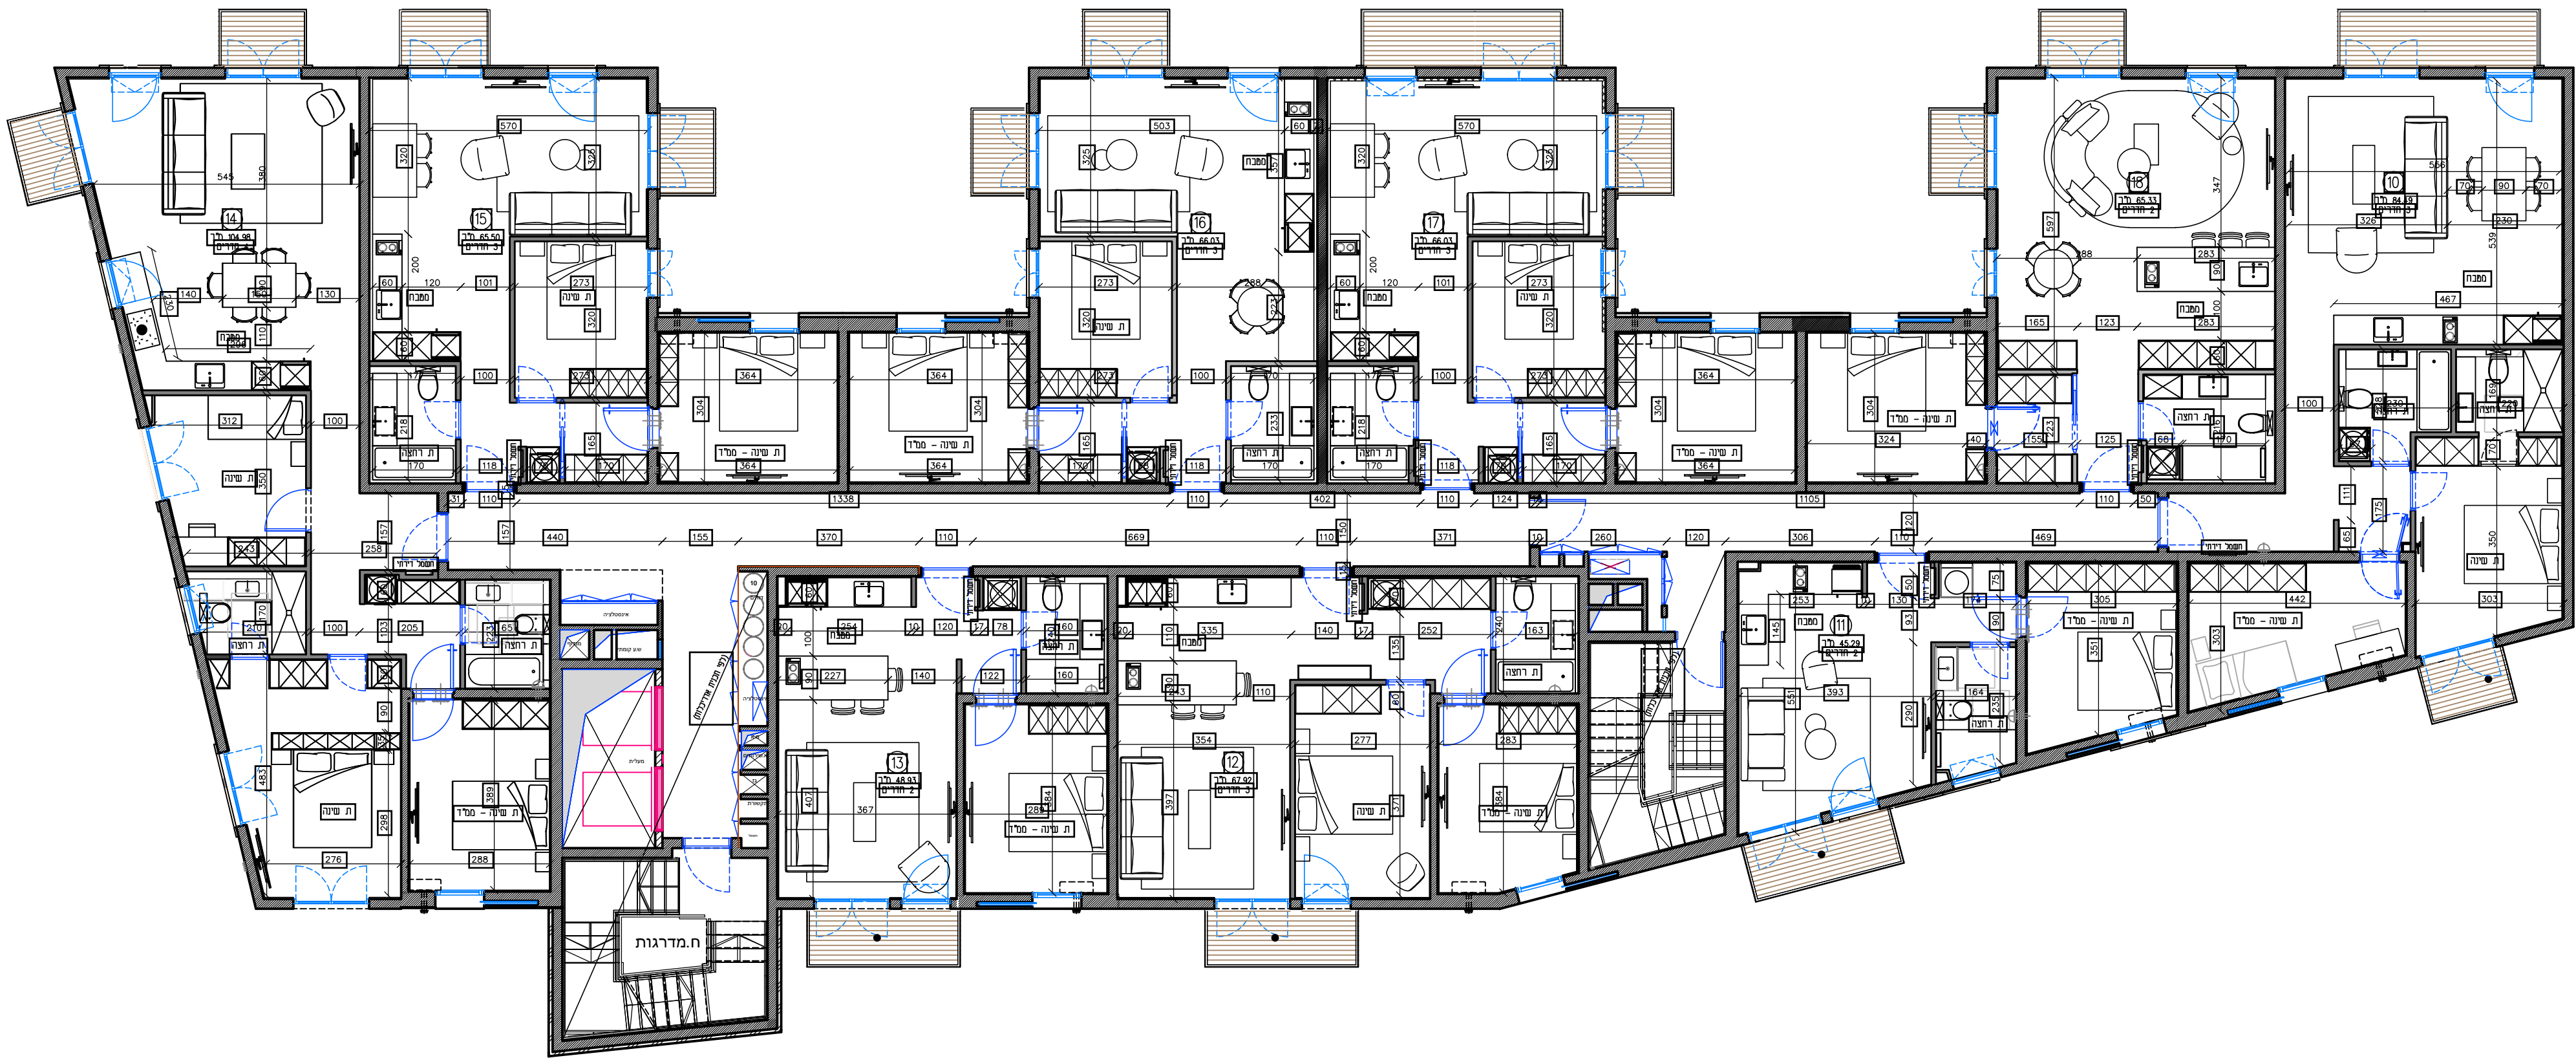

**YARON
ELDAD
ARCHI
TEC
TURE
+INTERIOR
DESIGN**

ירון אלדד
ארכיטקטורה ועיצוב פנים
כתובת: בובנישתי 11 ת"א
טלפון: 03-5335536/7
פקס: 03-5480136
yaroneldad.com

על הקבלן לבקר את המידות, להתאים לביצוע ולהודיע למחנך
על כל שנות, מסות, סחירה או אי התאמה בפרטים ימשיך עבודתו
המחנך יהיה הבעלים הנכסיו של חכנית זו ועל זכות הוצאים בה
אין לעשות כל שינוש בחכנית זו, בועיות והגזומים בה
כל אישור מראש ובכתב של המחנך.


מקרא:
קירות גבס/בלוקים
קירות חוק
עמודים

מס'	תאריך	שינויים
1		
2	07/07/2026	הזחת דלתות חדרי שינה
3		
4		

כביצוע	הפצה	תאריך
1	סלדורה	01
2	יזון אינדו אדיכל	02
3	מנהל פויקם	03
4	קונסטרוקטור	04
	יועץ חנוכה	
	איוטפציה	
	מיוג אירי	
	חושכל	
	ביוג, אשום ואקוסטיקה	
	בשיחוח	
	מעכיות	
	יועץ גל"א	
	יועץ גישות	
	קבלן	

07/07/2026	תאריך:
2	מחדורה:
1:100	קני"מ:
A2	גודל גליון:
יפו - תל אביב	כתובת:
קומה ב - דיהום	שם התוכנית:

שם הפרויקט:
הדואר 8

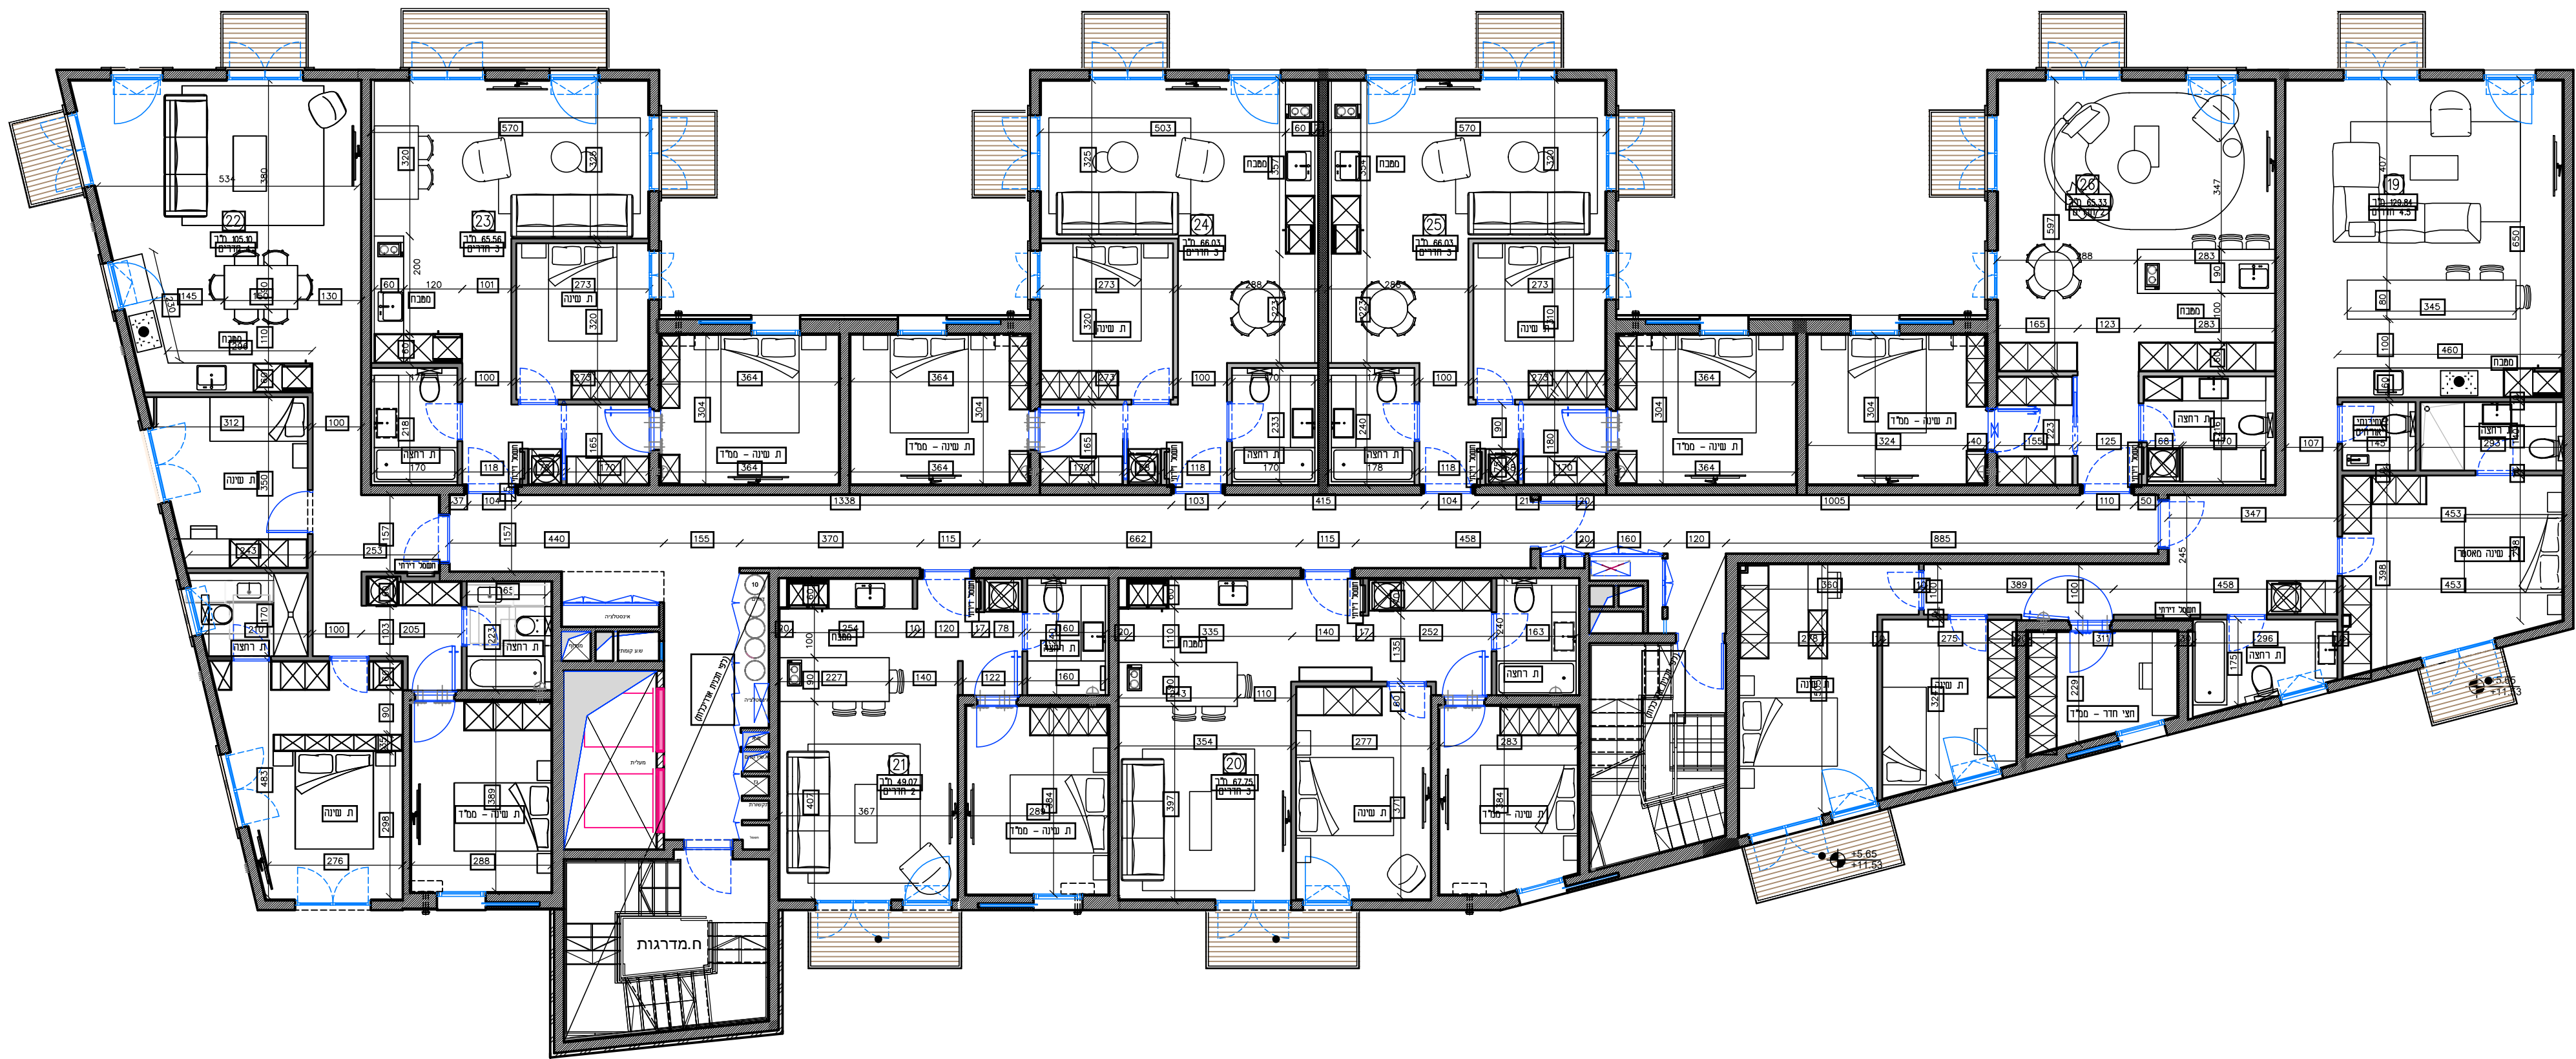

**YARON
ELDAD
ARCHI
TURE
+INTERIOR
DESIGN**

ירון אלדד
ארכיטקטורה ועיצוב פנים
כתובת: בובנישתי 11 ת"א
טלפון: 03-5335536/7
פקס: 03-5480136
yaroneldad.com

על הקבץ לבקר את המידות, להתאים לביצוע ולהודיע למחנך
על כל שעות, מספר, סחורה או אי התאמה בפרט ימשיך עבודתו
המחנך יהיה הבעלים הנכונים של חכמתו וזו ועל זכות הוציאים בה
אין לעשות כל שימוש בחכמתו, וזו, בפרטיות והגיונות בה
כל אישור מראש ובכתב של המחנך.

מקרא:
קירות גבס/בלוקים
קירות חוק
עמודים

ענייניים
תאריך
07/07/2026
הזאת דלתות חדרי שינה

כביצוע
למכרז
כאישור
כעיון

הפצה
סחורה
יחיד אידוכי
מנהל פרויקט
קונסטרוקטור
יועץ תכנון
איוטפציה
מיוג איר
הושק
ביוג, אשם ואקוסטיקה
ביטוח
מעבדות
יועץ ה"א
יועץ גישות
קבץ

תאריך: 07/07/2026
מחזור: 2
קנין: 1:100
גודל גליון: A2
שם הפרויקט: יהודא 8
כתובת: יפו - תל אביב
שם התוכנית: קומה ג - ריהוט